



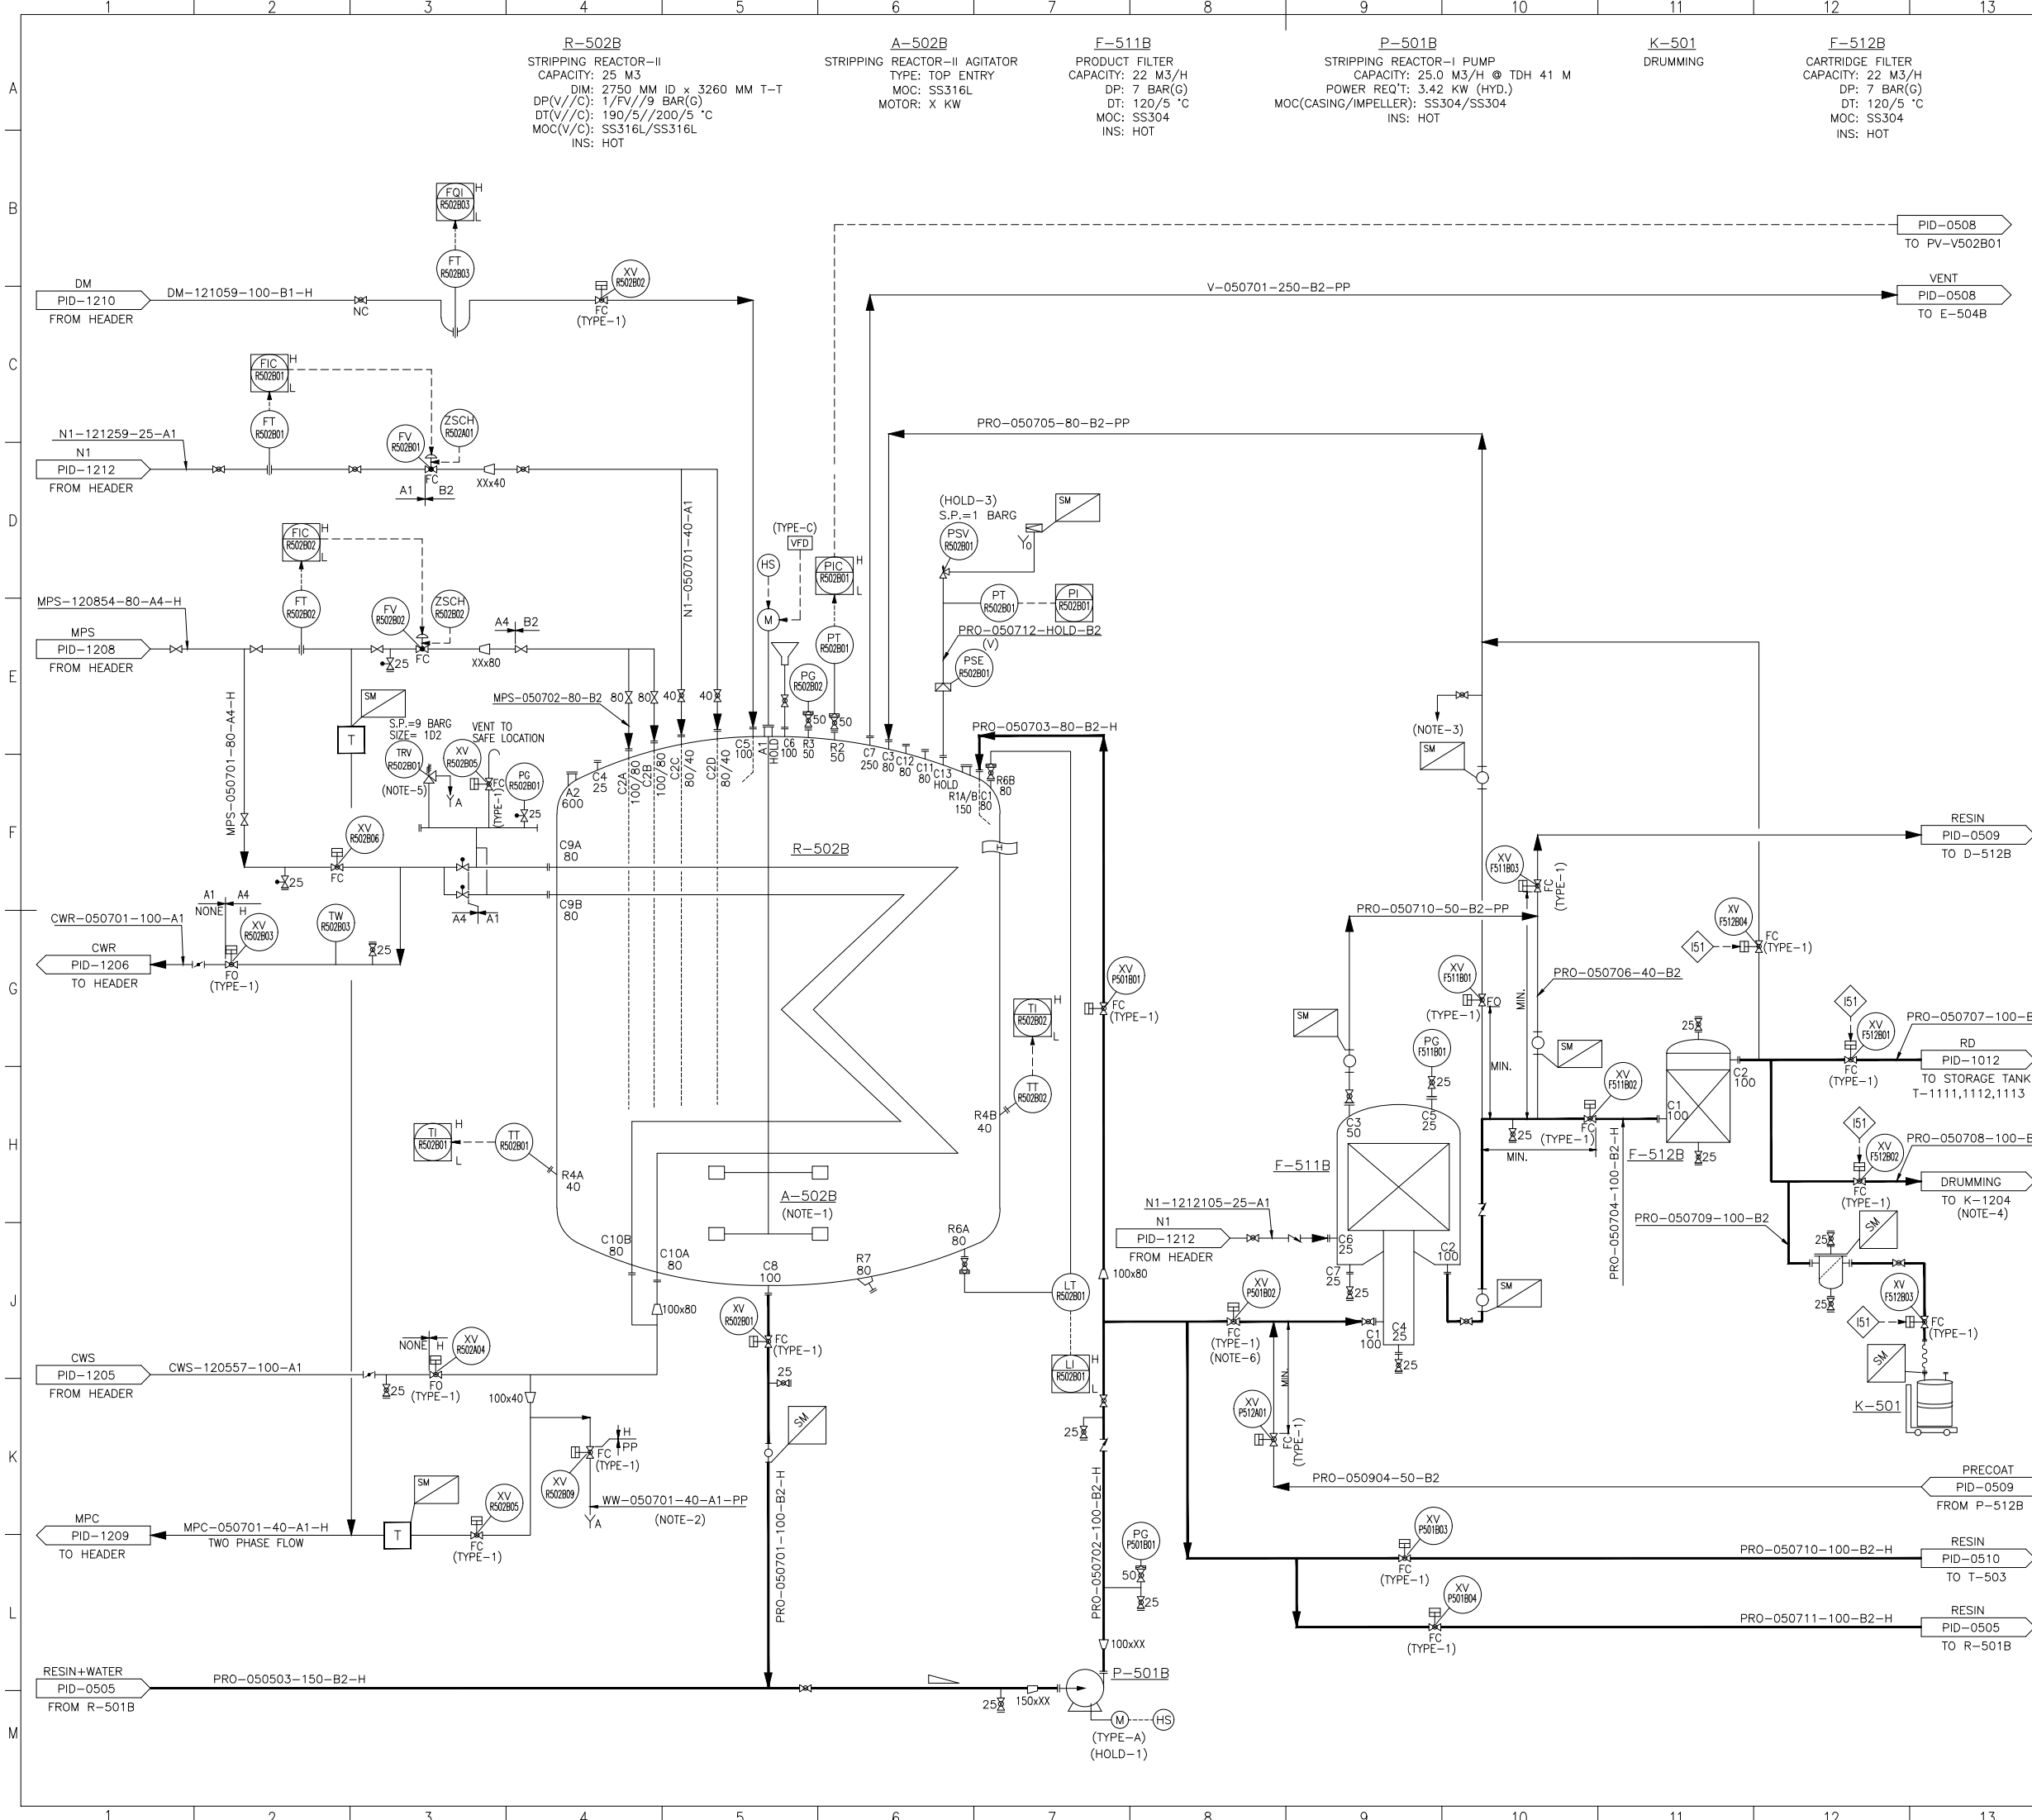

- GENERAL NOTES:**
- ALL VAPOR LINES, SLURRY LINES AND GRAVITY LINES SHOULD HAVE MINIMUM BENDS AND NO LOOPS.
 - PROVIDE PROPER EARTHING AND BONDING FOR THE HYDROCARBON LINES.
 - DELETED.
 - DRAIN TO BE PROVIDED AT THE LOWEST POINT AND VENT TO BE PROVIDED AT THE HIGHEST POINT.
 - REFER LEGEND SHEET FOR ABBREVIATIONS, SYMBOL, ON-OFF VALVE DETAILS, MOTOR/VFD AND STEAM TRAP DETAILS.
 - DWG NO. EPAM01-PR-PID-1000, EPAM01-PR-PID-1001, EPAM01-PR-PID-1002.
 - FOR LINES WITH SLOPE, SLOPE TO BE PROVIDED IN SUCH A WAY THAT THE LINE SHOULD BE DRAINED ON EITHER SIDE.
 - PROPOSED SPECIAL PIPING ITEM. TO BE FINALISED DURING DETAIL ENGINEERING.
 - TYPICAL XV SYMBOL ON PID TO BE READ AS BELOW.

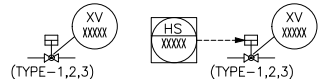

- FOR ALL INLINE INSTRUMENTS, UPSTREAM AND DOWNSTREAM DISTANCE TO BE CONSIDERED IN PIPING.
- ORIFICE TO BE INSTALLED IN HORIZONTAL LINE ONLY.
- INSTRUMENT ISOLATION VALVES & DRAIN/VENT REQUIREMENT TO BE UPDATED DURING DETAILED DESIGN ALONG WITH THE P&ID.

- NOTES:**
- AGITATOR MOTOR SHALL TRIP FROM DCS IN CASE OF MECHANICAL SEAL LEAKAGE.
 - ALL DRAIN POINTS SHALL BE CONNECTED TO A SEPARATE HEADER.
 - SAMPLE POINT PROVISION, SAMPLE TO BE COLLECTED MANUALLY.
 - DRUMMING IN WAREHOUSE.
 - FUNNEL ARRANGEMENT AND ROUTING TO BE DONE DURING DETAILED ENGINEERING.
 - XV-P501B02 SHOULD BE NEAR TO T POINT.

- HOLDS:**
- PUMP SUCTION AND DISCHARGE NOZZLE SIZE.
 - FILTER NOZZLE DETAILS.
 - PSV SIZE.

INTERLOCK TABLE:

NO.	CAUSE	EFFECT
151	IF ONE XV OPEN OF XV-F512B01/XV-F512B02/XV-F512B03/XV-F512B04	OTHER XVs REMAIN CLOSED

0	01-JUN-26	ISSUED FORDETAIL ENGG.	DVS	NC	DP	KV
B	29-MAY-26	ISSUED FOR DESIGN	DVS	NC	DP	KV
A	27-MAR-26	ISSUED FOR APPROVAL	DVS	NC	DP	KV
No.	DATE	REVISION	DRAWN	CHD	REVD	APPD

**Rasayan Engineering Solutions**

CLIENT:
 **EPIGRAL Limited**

PROJECT:
BASIC ENGINEERING FOR EPAM PROJECT

TITLE:
PIPING & INSTRUMENTATION DIAGRAM STRIPPING REACTION & FILTRATION SECTION (RD) TRAIN-II

SCALE : NTS | DWG.NO.:EPAM01-PR-PID-0507 | SHT: 1 OF 1 | REV. 0